
A house organized around its rear patio

3 bedrooms / 3 bathrooms / 8 guests / 1 car | Furnished schematic, meters | A3 at 1:100 when printed at 100%

01 GROUND FLOOR



02 UPPER FLOOR

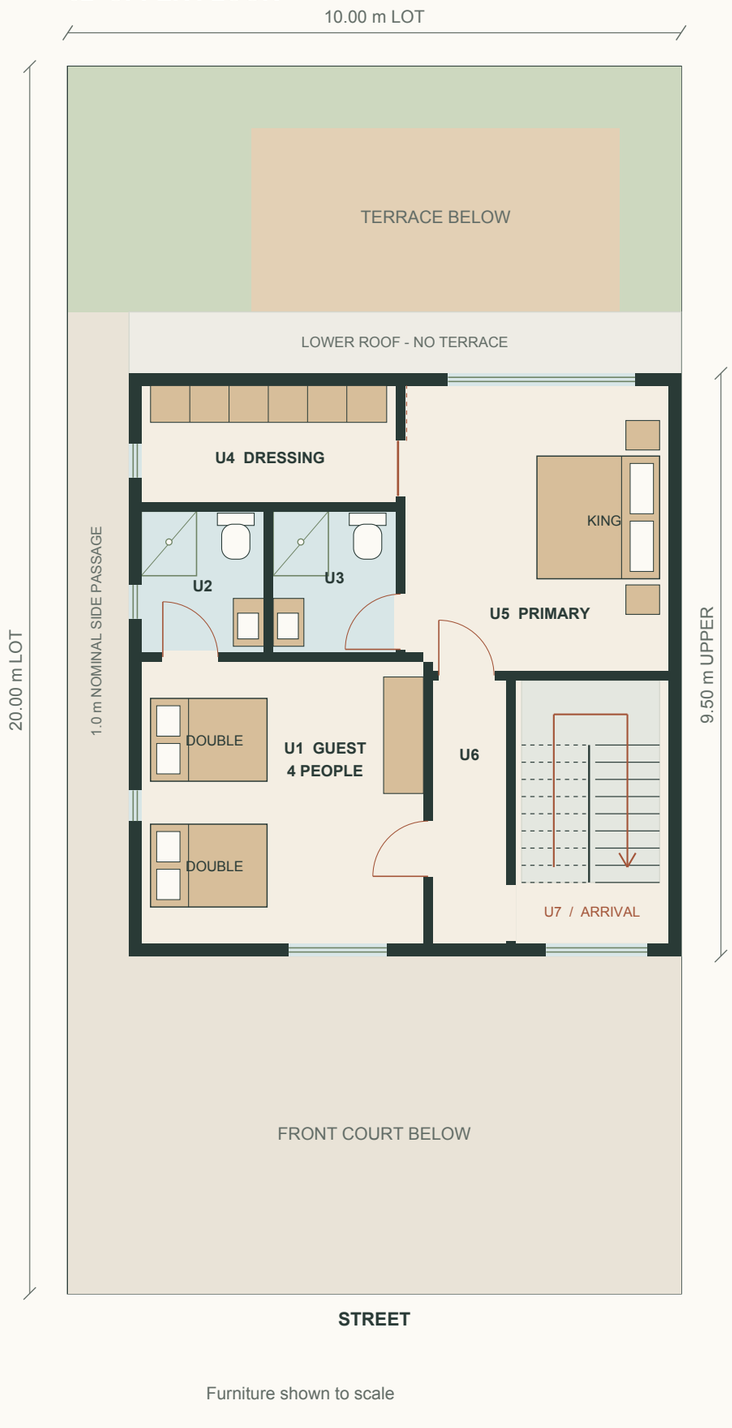



The agreed brief

Two floors, a downstairs queen guest room, an upstairs king primary suite, and an upstairs room with two double beds. Three full bathrooms. Warm Mexican contemporary finishes.

The proposed fit

Ground floor	94.5 m²
Upper, stair void deducted	78.1 m²
Combined floor area	172.6 m²
Covered rear terrace, extra	18.0 m²

Floor areas use exterior wall faces. They include walls and circulation. The 7.4 m² upper stair opening is deducted; this is not the municipal area calculation.

Room arrangement

Ground / social + guest

G1 queen room; G2 shared bath; G3 laundry from the side passage; G4 L-shaped kitchen; G5 lounge and eight-place dining; G6 entry; G7 stair.

Upper / private

U1 two-double guest room; U2 its private bath; U3 primary bath; U4 dressing/storage; U5 primary bedroom; U6 hall; U7 stair arrival.

What this drawing does not fix

Setbacks, boundary-wall permission, floor elevation, structural design and utility arrangements remain open. Front/rear orientation is schematic; no surveyed north direction is asserted.

Area, circulation and budget checks

Planning allowances and geometry checks - no local construction quotation or code-compliance determination

Where the 200 m² lot goes

Main ground-floor footprint	94.5 m²
Front parking / entrance zone	55.0 m²
Nominal side passage	10.5 m²
Rear outdoor zone (18 covered + 22 uncovered)	40.0 m²
Total lot allocation	200.0 m²

Approximate internal room sizes

Ground queen room	3.60 x 4.10 m / 14.8 m²
Ground shared bath	1.85 x 2.30 m / 4.3 m²
Laundry	1.60 x 2.30 m / 3.7 m²
Living + dining rectangle	8.60 x 3.40 m / 29.2 m²
Kitchen / transition zone	4.85 x 2.10 m / 10.2 m²
Upper two-double guest room	4.60 x 4.60 m / 21.2 m²
Each upstairs bathroom	2.00 x 2.30 m / 4.6 m²
Primary bedroom, excluding entry nook	4.30 x 4.35 m / 18.7 m²
Primary dressing / storage	4.15 x 1.90 m / 7.9 m²

Room rectangles are internal planning zones, not a second gross-area total. Kitchen and lounge connect through open circulation. Actual cabinetry, services, wall finishes and purchased furniture must be checked during design development.

Furniture and use checks

Queen: 1.52 x 2.03 m. King: 2.00 x 2.00 m. Doubles: 1.35 x 1.90 m each. Eight guests means two people share each double bed. Indoor table: 2.20 x 0.95 m, eight chairs. The lounge uses an L-sofa and two armchairs; dining chairs can supplement it.


Laundry access is outdoors through the side passage. The dressing room is the first space to compress in a smaller alternative. The right boundary wall has no windows or doors.

Local cost planning

Construction + site works	Local quote
Design, studies and permits	Local quote
Furniture and appliances	Local quote
Contingency	To be assessed
Total, excluding land	To be priced

Costs require local pricing for the house, terrace, installed kitchen/joinery, drainage, services, boundaries and gate. Obtain comparable itemized quotations before committing to construction.

Stair fit study

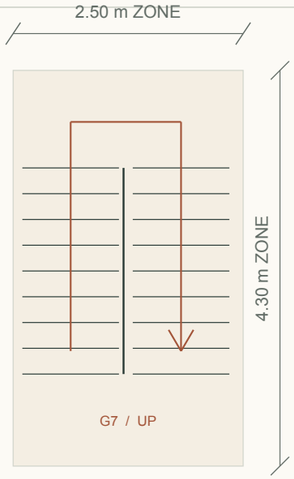

18 risers / 9 per flight
175 mm riser at a provisional 3.15 m floor-to-floor height
280 mm treads / 2.24 m run per flight
1.05 m nominal flights and turning landing
1.00 m front arrival landing

The area and tread arithmetic fit the reserved zone. Headroom, handrails/guards, clear widths after finishes, structural support and local compliance still require architectural and engineering review.

Decision before design development

Obtain local pricing against this exact scope before accepting the floor area. If the total exceeds the target, simplify discretionary finishes and joinery, then test a smaller furnished plan. Preserve the patio, bathroom usefulness, drainage and waterproofing.

Warm, private and easy to return to

Appearance study / warm cream plaster, terracotta screen, restrained tilework and shaded outdoor living





AI-generated appearance reference using the built-in image tool. It conveys materials, shade and massing; window positions, roof supports, planting and apparent distances are illustrative. The measured schematic governs the proposed geometry.

01 / Confirm the envelope

Commission a boundary/topographic survey and obtain the parcel-specific municipal conditions. This concept depends on a side-boundary wall, a one-meter side passage and a covered terrace.

02 / Establish the site levels

Use a parcel-level drainage/flood assessment and geotechnical advice to set floor elevation and foundations. Confirm water, sewer and electrical connections before fixing equipment or service space.

03 / Price the same scope

Ask local professionals to price the same room schedule, finishes and inclusions. Separate tax, fees, furnishings, site works and contingency; resolve exclusions before approving design development.

Basis: client brief; municipal land-use requirements; 2014 municipal risk atlas.