

# Three bedrooms. Two bathrooms. Better separation.

Shared full bathroom on each floor / 8 guests / 1 car | Furnished schematic, meters | A3 at 1:100 when printed at 100%

## 01 GROUND FLOOR

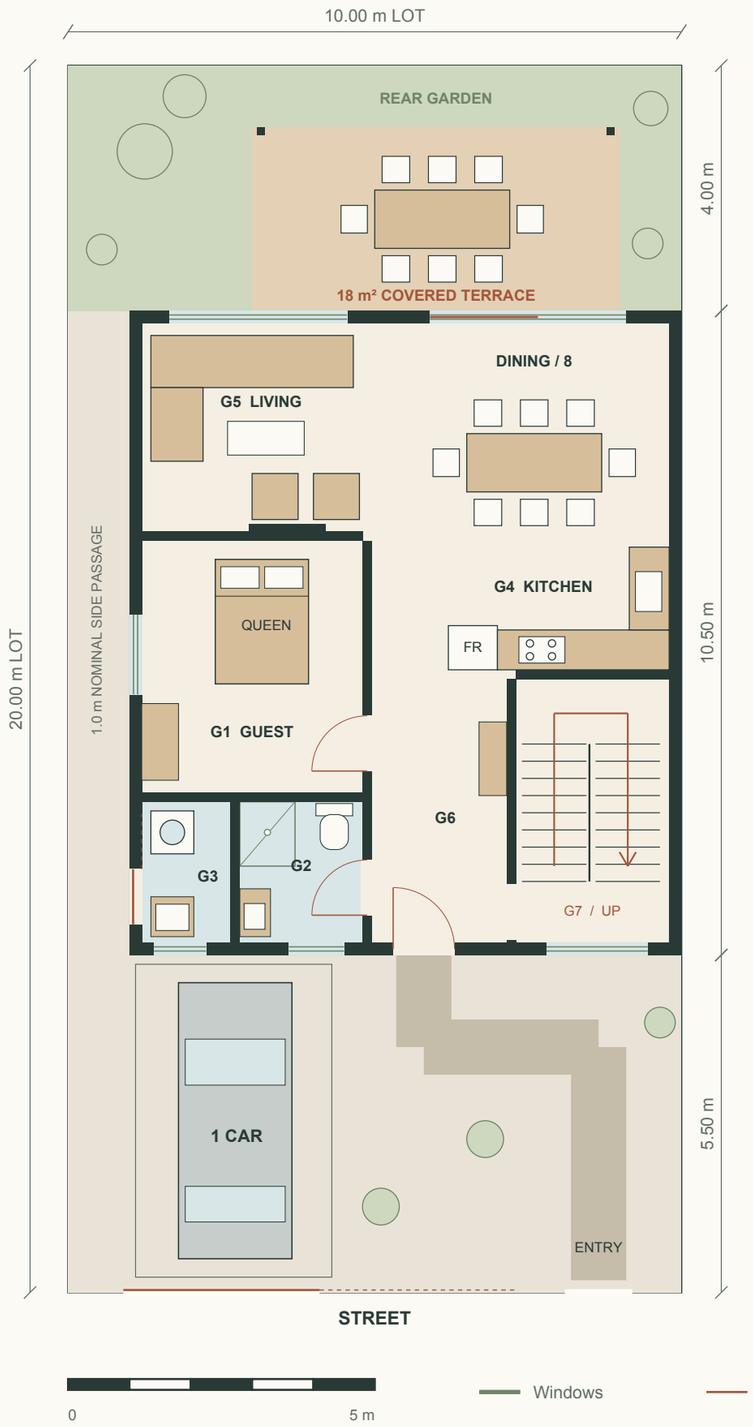


## 02 UPPER FLOOR

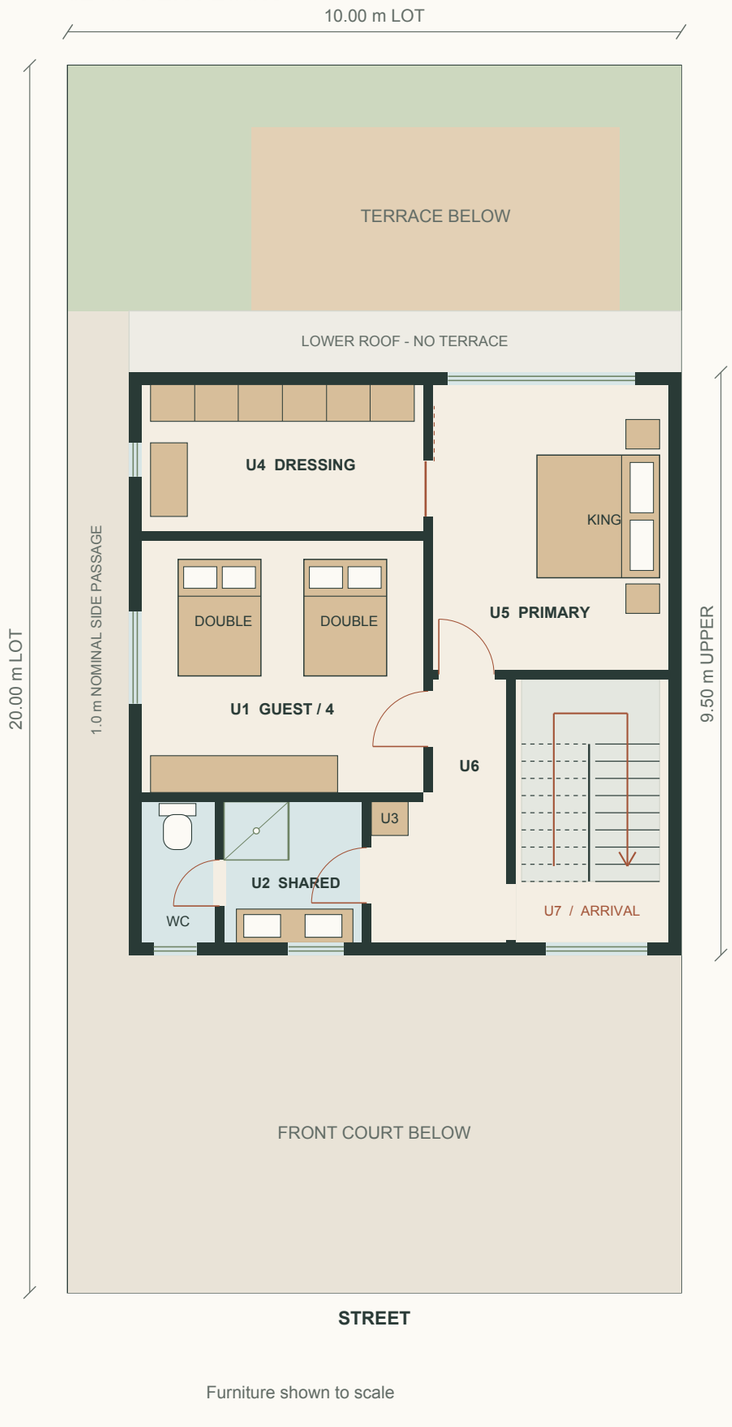


0 5 m — Windows — Door swings — Furniture shown to scale

## 3 bedrooms / 2 full bathrooms

Queen guest room downstairs; king primary and two-double guest room upstairs. Each floor has one shared, hall-accessed bathroom. Neither bedroom upstairs is an en suite.

## The proposed fit

| SPACE / ITEM | m² | ft² / ref. |
|---|---|---|
| Ground floor | 94.5 m² | 1,017.2 ft² |
| Upper, less stair void | 78.1 m² | 840.6 ft² |
| Combined floors | 172.6 m² | 1,857.8 ft² |
| Covered terrace, extra | 18.0 m² | 193.8 ft² |

Areas include exterior walls and circulation; the upper stair opening is deducted. Municipal area rules may differ. Feet are rounded references; metric dimensions govern.

## Bathroom separated from kitchen

G2 is at the front, off the entry hall. It shares no wall with the kitchen. The bedroom and circulation form a buffer, with 2.0 m of plan-depth separation from the bathroom rear wall to the kitchen zone.

## Room arrangement

### Ground / social + guest

G1 queen room; G2 front shared bath; G3 front laundry from side passage; G4 kitchen; G5 living/dining; G6 entry; G7 stair.

### Upper / shared bath

U1 two-double room; U2 shared bath with double vanity and separate toilet compartment; U3 linen; U4 dressing/storage; U5 primary; U6 hall; U7 stair arrival.

## Still schematic

Setbacks, boundary-wall permission, floor elevation, structure and services need local review. Front/rear orientation is schematic; no surveyed north is asserted.

# Area, circulation and budget checks

Metric dimensions govern. Feet are decimal and rounded for reference. Areas are shown in square meters and square feet.

## Where the 200 m² lot goes

| SPACE / ITEM | Square meters / m² | Square feet / ft² |
|---|---|---|
| Main ground-floor footprint | 94.5 m² | 1,017.2 ft² |
| Front parking / entrance | 55.0 m² | 592.0 ft² |
| Nominal side passage | 10.5 m² | 113.0 ft² |
| Rear outdoor zone | 40.0 m² | 430.6 ft² |
| Total lot allocation | 200.0 m² | 2,152.8 ft² |

## Approximate internal room sizes

| SPACE / ITEM | Meters | Feet / reference |
|---|---|---|
| G1 / Ground queen room | 3.60 x 4.10 m<br>14.8 m² | 11.81 x 13.45 ft<br>158.9 ft² |
| G2 / Ground shared bath / front | 2.00 x 2.30 m<br>4.6 m² | 6.56 x 7.55 ft<br>49.5 ft² |
| G3 / Front laundry | 1.45 x 2.30 m<br>3.3 m² | 4.76 x 7.55 ft<br>35.9 ft² |
| G5 / Living + dining | 8.60 x 3.40 m<br>29.2 m² | 28.22 x 11.15 ft<br>314.7 ft² |
| G4 / Kitchen / transition | 4.85 x 2.10 m<br>10.2 m² | 15.91 x 6.89 ft<br>109.6 ft² |
| U1 / Upper two-double room | 4.60 x 4.10 m<br>18.9 m² | 15.09 x 13.45 ft<br>203.0 ft² |
| U2 / Upper shared bath, incl. WC | 3.60 x 2.30 m<br>8.3 m² | 11.81 x 7.55 ft<br>89.1 ft² |
| U5 / Primary bedroom | 3.85 x 4.65 m<br>17.9 m² | 12.63 x 15.26 ft<br>192.7 ft² |
| U4 / Primary dressing / storage | 4.60 x 2.40 m<br>11.0 m² | 15.09 x 7.87 ft<br>118.8 ft² |

Each room row shows width x depth, with area beneath. These are internal planning zones; do not add them as a gross-floor total. Conversions use the unrounded metric values. Rear outdoor space includes the covered terrace and uncovered patio.

## Privacy and everyday use

Both full bathrooms open from the hall. The upstairs WC compartment belongs to the shared bathroom. Use privacy glazing at front wet-room windows; access laundry from the side passage. Eight guests assumes two people share each double bed.

## Local cost planning

| | |
|---|---|
| Construction + site works | Local quote |
| Design, studies and permits | Local quote |
| Furniture and appliances | Local quote |
| Contingency | To be assessed |
| Total, excluding land | To be priced |

Provisional allowances, excluding land; no local quotation. Reprice the two-bathroom layout before assuming savings or accepting the floor area. If over target, simplify discretionary finishes and joinery first; preserve drainage, waterproofing and the patio.

## Furniture and stair references

| SPACE / ITEM | Meters | Feet / reference |
|---|---|---|
| Lot / frontage x depth | 10.00 x 20.00 m | 32.81 x 65.62 ft |
| Queen mattress | 1.52 x 2.03 m | 4.99 x 6.66 ft |
| King mattress | 2.00 x 2.00 m | 6.56 x 6.56 ft |
| Each double mattress | 1.35 x 1.90 m | 4.43 x 6.23 ft |
| Dining table / eight seats | 2.20 x 0.95 m | 7.22 x 3.12 ft |
| Reserved stair zone | 2.50 x 4.30 m | 8.20 x 14.11 ft |
| Provisional floor-to-floor | 3.15 m | 10.33 ft |
| Riser / 18 total, 9 per flight | 0.175 m | 0.57 ft |
| Tread depth | 0.280 m | 0.92 ft |
| Run per flight / 8 treads | 2.24 m | 7.35 ft |
| Flight / turning landing | 1.05 m | 3.44 ft |
| Front arrival landing | 1.00 m | 3.28 ft |

Stair arithmetic fits the reserved zone. Headroom, guards, finished clear widths, structure and local compliance need professional review. Furniture and cabinetry remain subject to selection and clearance checks.

# The same warm architectural character

Style reference retained from concept 01 / facade openings and privacy glazing to follow the revised plans







Earlier AI-generated style reference, retained for materials and massing only. It has not been regenerated for the bathroom relocation. Front wet-room openings now need privacy glazing; use the revised floor plans for the room arrangement.

## 01 / Confirm the envelope

Commission a boundary/topographic survey and obtain the parcel-specific municipal conditions. This concept depends on a side-boundary wall, a one-meter side passage and a covered terrace.

## 02 / Establish the site levels

Use a parcel-level drainage/flood assessment and geotechnical advice to set floor elevation and foundations. Confirm water, sewer and electrical connections before fixing equipment or service space.

## 03 / Price the same scope

Ask local professionals to price the same room schedule, finishes and inclusions. Separate tax, fees, furnishings, site works and contingency; resolve exclusions before approving design development.

Basis: client brief; municipal land-use requirements; 2014 municipal risk atlas.