
Indoor access to laundry and bathroom.

Shared full bathroom on each floor / 8 guests / 1 car | Furnished schematic, meters | A3 at 1:100 when printed at 100%

01 GROUND FLOOR



02 UPPER FLOOR

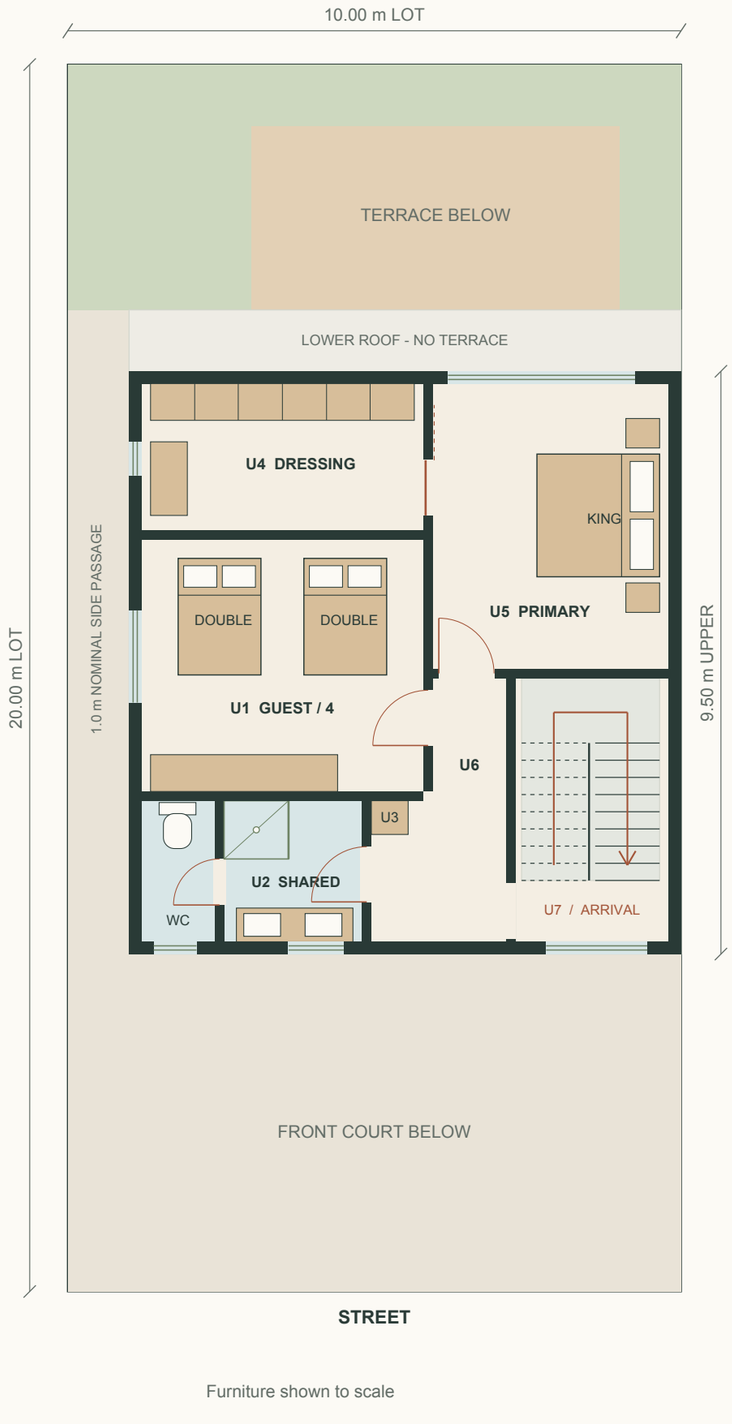

0 5 m — Windows — Door swings — Furniture shown to scale

3 bedrooms / 2 full bathrooms

Queen guest room downstairs; king primary and two-double guest room upstairs. Each floor has one shared, hall-accessed bathroom. Neither bedroom upstairs is an en suite.

The proposed fit

SPACE / ITEM	m²	ft² / ref.
Ground floor	94.5 m²	1,017.2 ft²
Upper, less stair void	78.1 m²	840.6 ft²
Combined floors	172.6 m²	1,857.8 ft²
Covered terrace, extra	18.0 m²	193.8 ft²

Areas include exterior walls and circulation; the upper stair opening is deducted. Municipal area rules may differ. Feet are rounded references; metric dimensions govern.

Your swap, with an indoor passage

G2 moves to the left; G3 sits beside the entry hall. G8 provides a 1.00 m / 3.28 ft-wide route behind the recessed laundry bay to the bathroom. The bathroom remains buffered from the kitchen. See the enlarged plan on page 2.

Room arrangement

Ground / social + guest

G1 queen room; G2 front shared bath; G3 stacked laundry bay; G4 kitchen; G5 living/dining; G6 entry; G7 stair; G8 indoor passage.

Upper / shared bath


U1 two-double room; U2 shared bath with double vanity and separate toilet compartment; U3 linen; U4 dressing/storage; U5 primary; U6 hall; U7 stair arrival.

Still schematic

Setbacks, boundary-wall permission, floor elevation, structure and services need local review. Front/rear orientation is schematic; no surveyed north is asserted.

A short indoor passage solves the access problem.

Enlarged ground-floor service area / 1:25 on A3 at 100% / meter and feet reference columns below

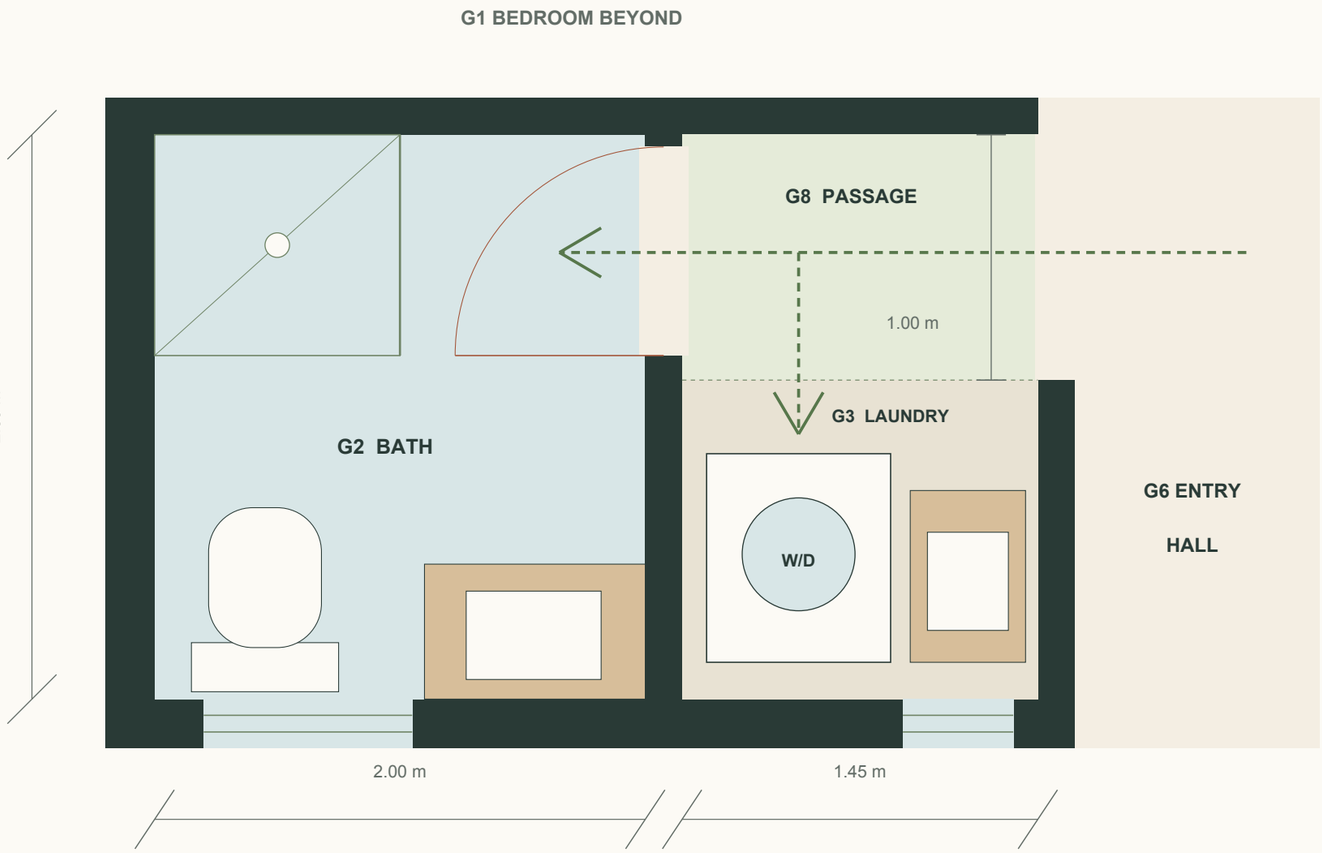

Service-area dimensions

SPACE / ITEM	Meters	Feet / reference
G2 / Bathroom	2.00 x 2.30 m	6.56 x 7.55 ft
G3 / Recessed laundry bay	1.45 x 1.30 m	4.76 x 4.27 ft
G8 / Passage	1.45 x 1.00 m	4.76 x 3.28 ft

Dashed green arrows show indoor access. The laundry bay includes appliance/service depth; the passage is a separate circulation zone.

Entry hall > passage > bathroom

Turn left from G6 into the short G8 passage. The bathroom door is at the end. The stacked washer/dryer faces this same passage from the recessed G3 bay, so both are reached indoors.

A swap with one partition adjustment

Move the dividing wall so the bathroom keeps its 2.00 x 2.30 m footprint. The remaining 1.45 m-wide bay holds the stacked laundry at the front and the 1.00 m-wide passage behind it.

What this layout assumes

Stacked appliances and an open laundry alcove are shown. Appliance depth, hose space, drainage, dryer ventilation and any future enclosure need to follow the selected equipment. Loading laundry temporarily uses part of the passage.

The door stays inside the bathroom

The nominal 0.85 m / 2.79 ft door swings into G2, away from the passage. The exterior laundry entrance is removed. The bathroom still shares no wall with the kitchen; the bedroom and circulation remain between them.

Dimensions are schematic planning targets, not a clearance or accessibility certification. Final wall finishes, fixtures and door hardware need detailed review.

Area, circulation and budget checks

Metric dimensions govern. Feet are decimal and rounded for reference. Areas are shown in square meters and square feet.

Where the 200 m² lot goes

SPACE / ITEM	Square meters / m²	Square feet / ft²
Main ground-floor footprint	94.5 m²	1,017.2 ft²
Front parking / entrance	55.0 m²	592.0 ft²
Nominal side passage	10.5 m²	113.0 ft²
Rear outdoor zone	40.0 m²	430.6 ft²
Total lot allocation	200.0 m²	2,152.8 ft²

Approximate internal room sizes

SPACE / ITEM	Meters	Feet / reference
G1 / Ground queen room	3.60 x 4.10 m 14.8 m²	11.81 x 13.45 ft 158.9 ft²
G2 / Ground shared bath / front	2.00 x 2.30 m 4.6 m²	6.56 x 7.55 ft 49.5 ft²
G3 / Recessed laundry bay	1.45 x 1.30 m 1.9 m²	4.76 x 4.27 ft 20.3 ft²
G5 / Living + dining	8.60 x 3.40 m 29.2 m²	28.22 x 11.15 ft 314.7 ft²
G4 / Kitchen / transition	4.85 x 2.10 m 10.2 m²	15.91 x 6.89 ft 109.6 ft²
U1 / Upper two-double room	4.60 x 4.10 m 18.9 m²	15.09 x 13.45 ft 203.0 ft²
U2 / Upper shared bath, incl. WC	3.60 x 2.30 m 8.3 m²	11.81 x 7.55 ft 89.1 ft²
U5 / Primary bedroom	3.85 x 4.65 m 17.9 m²	12.63 x 15.26 ft 192.7 ft²
U4 / Primary dressing / storage	4.60 x 2.40 m 11.0 m²	15.09 x 7.87 ft 118.8 ft²

Each room row shows width x depth, with area beneath. These are internal planning zones; do not add them as a gross-floor total. Conversions use the unrounded metric values. Rear outdoor space includes the covered terrace and uncovered patio.

Privacy and everyday use

Both full bathrooms have indoor shared access. Laundry opens to the new G8 passage; its separate area is 1.45 m² / 15.6 ft². Use privacy glazing at front wet-room windows. Eight guests assumes two people share each double bed.

Local cost planning

Construction + site works	Local quote
Design, studies and permits	Local quote
Furniture and appliances	Local quote
Contingency	To be assessed
Total, excluding land	To be priced

Provisional allowances, excluding land; no local quotation. Reprice the two-bathroom layout before assuming savings or accepting the floor area. If over target, simplify discretionary finishes and joinery first; preserve drainage, waterproofing and the patio.

Furniture and stair references

SPACE / ITEM	Meters	Feet / reference
Lot / frontage x depth	10.00 x 20.00 m	32.81 x 65.62 ft
Queen mattress	1.52 x 2.03 m	4.99 x 6.66 ft
King mattress	2.00 x 2.00 m	6.56 x 6.56 ft
Each double mattress	1.35 x 1.90 m	4.43 x 6.23 ft
Dining table / eight seats	2.20 x 0.95 m	7.22 x 3.12 ft
Reserved stair zone	2.50 x 4.30 m	8.20 x 14.11 ft
Provisional floor-to-floor	3.15 m	10.33 ft
Riser / 18 total, 9 per flight	0.175 m	0.57 ft
Tread depth	0.280 m	0.92 ft
Run per flight / 8 treads	2.24 m	7.35 ft
Flight / turning landing	1.05 m	3.44 ft
Front arrival landing	1.00 m	3.28 ft

Stair arithmetic fits the reserved zone. Headroom, guards, finished clear widths, structure and local compliance need professional review. Furniture and cabinetry remain subject to selection and clearance checks.

The same warm architectural character

Style reference retained from concept 01 / facade openings and privacy glazing to follow the revised plans





Earlier AI-generated style reference, retained for materials and massing only. It has not been regenerated for the bathroom/laundry swap. Front wet-room openings need privacy glazing; use the revised floor plans for the room arrangement.

01 / Confirm the envelope

Commission a boundary/topographic survey and obtain the parcel-specific municipal conditions. This concept depends on a side-boundary wall, a one-meter side passage and a covered terrace.

02 / Establish the site levels

Use a parcel-level drainage/flood assessment and geotechnical advice to set floor elevation and foundations. Confirm water, sewer and electrical connections before fixing equipment or service space.

03 / Price the same scope

Ask local professionals to price the same room schedule, finishes and inclusions. Separate tax, fees, furnishings, site works and contingency; resolve exclusions before approving design development.

Basis: client brief; municipal land-use requirements; 2014 municipal risk atlas.